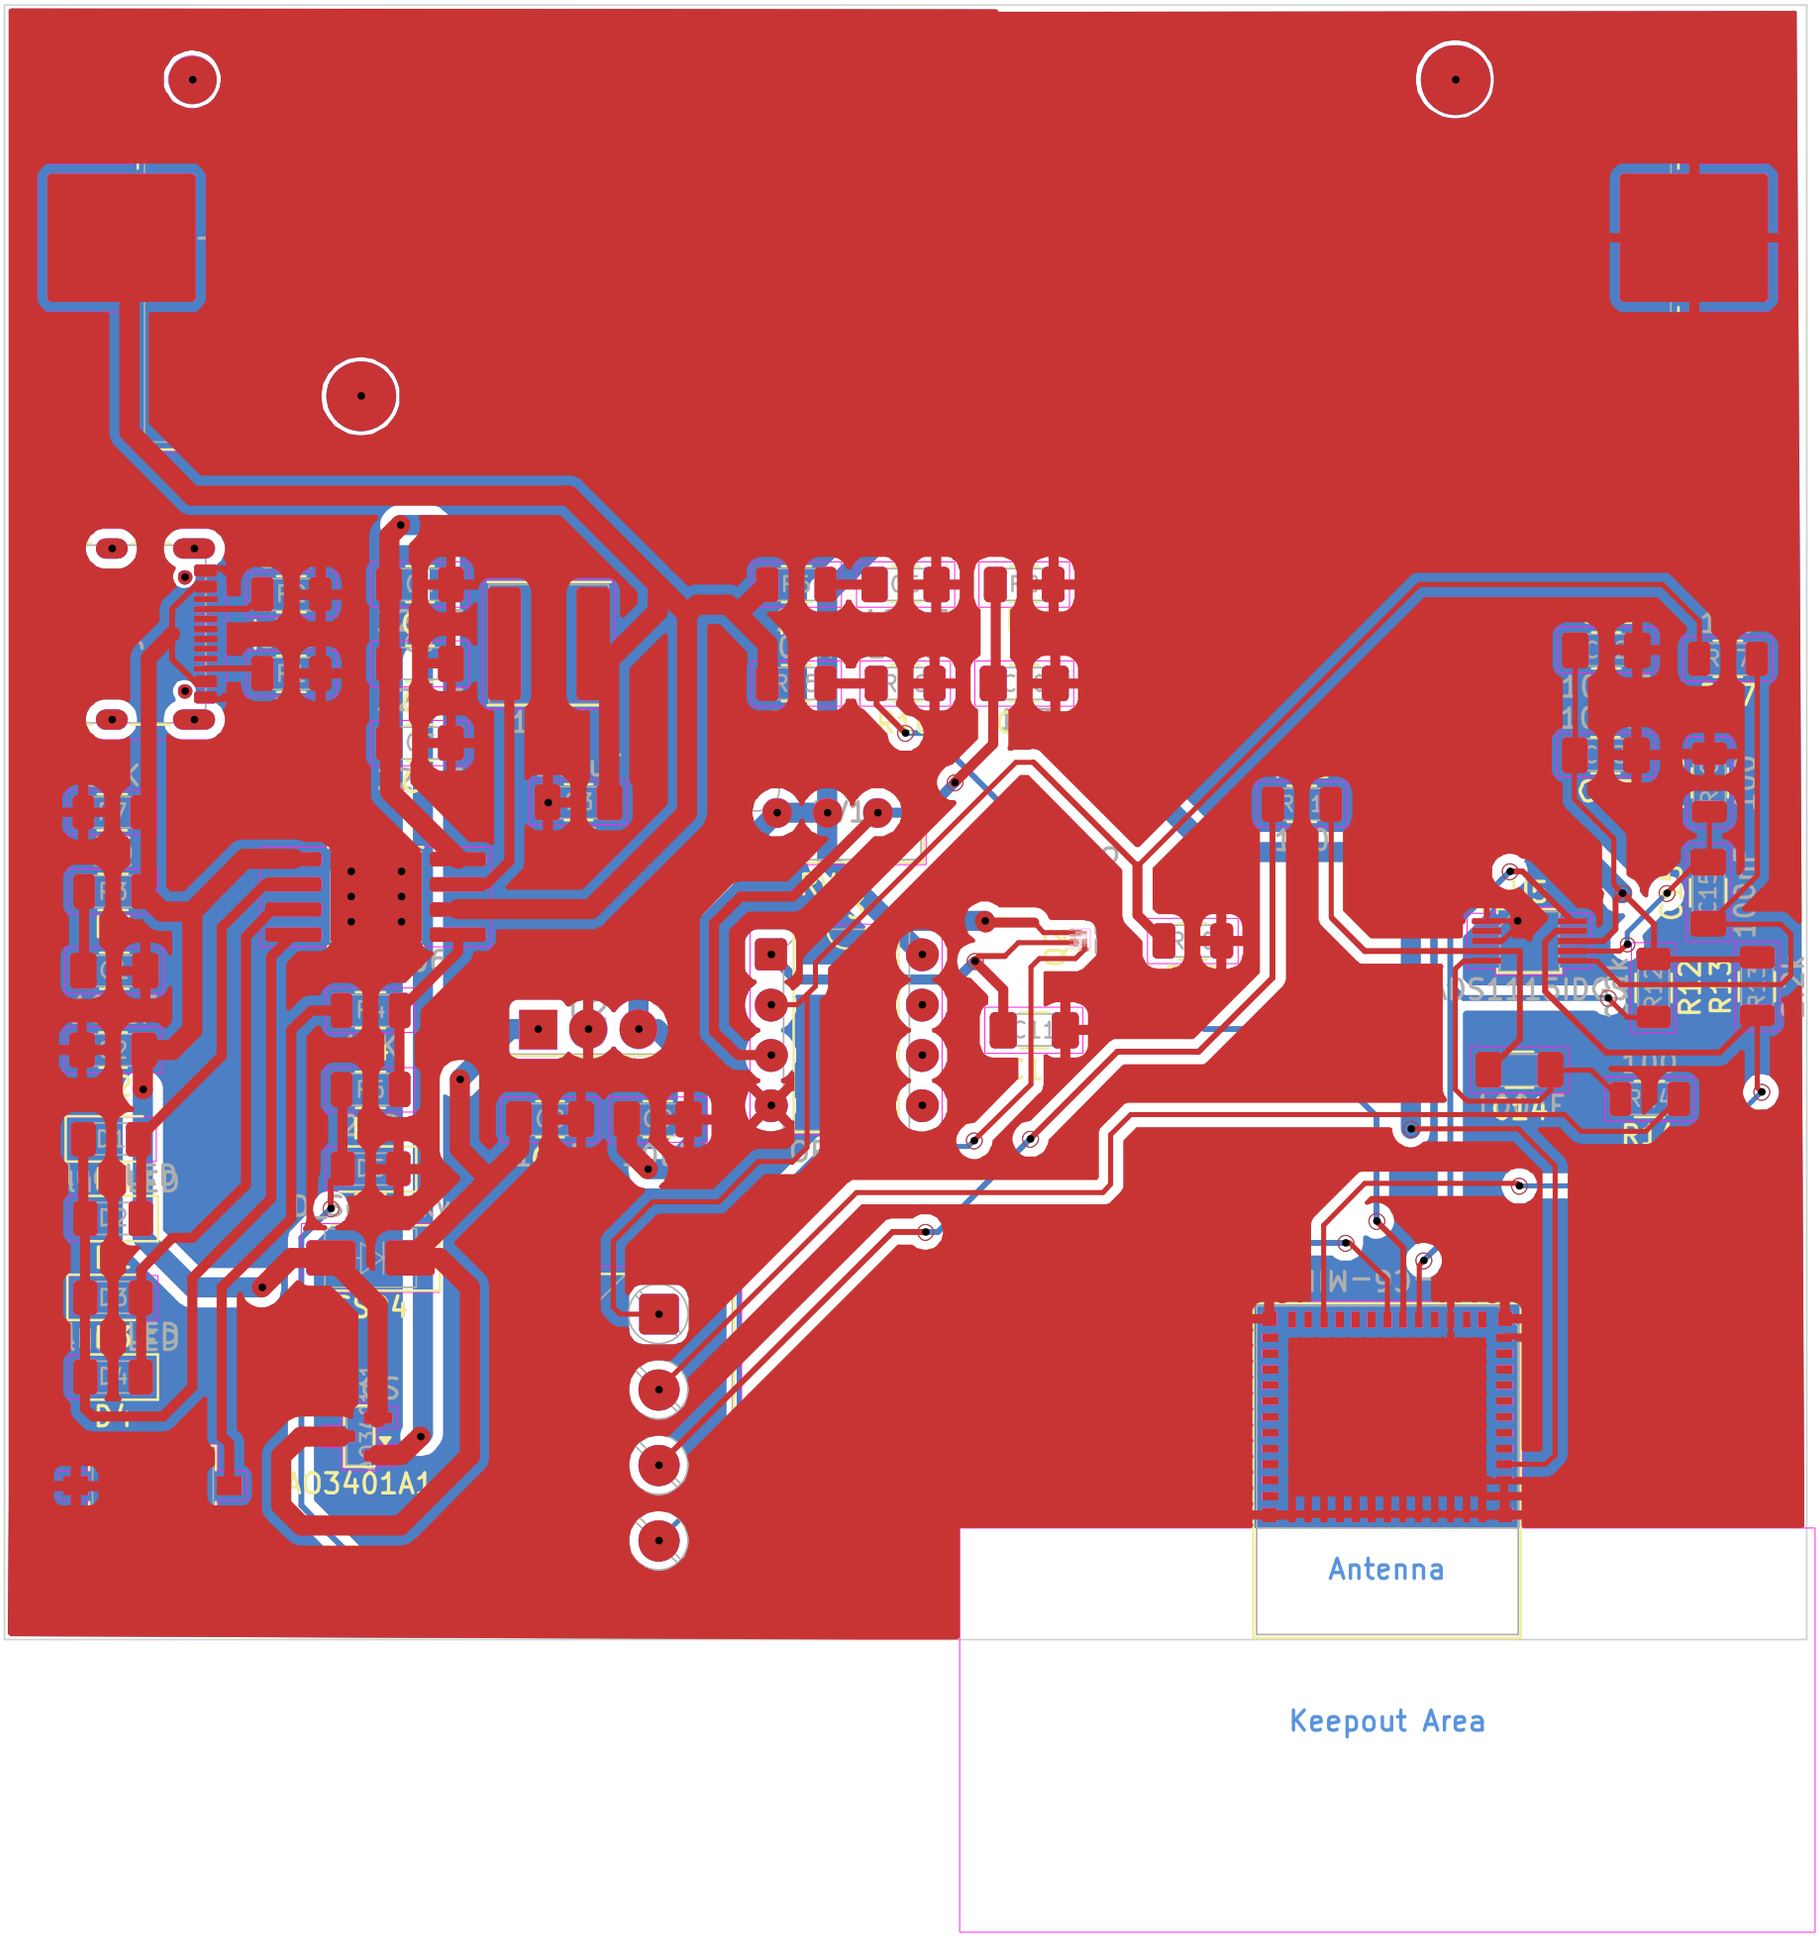

Antenna
Keepout Area